


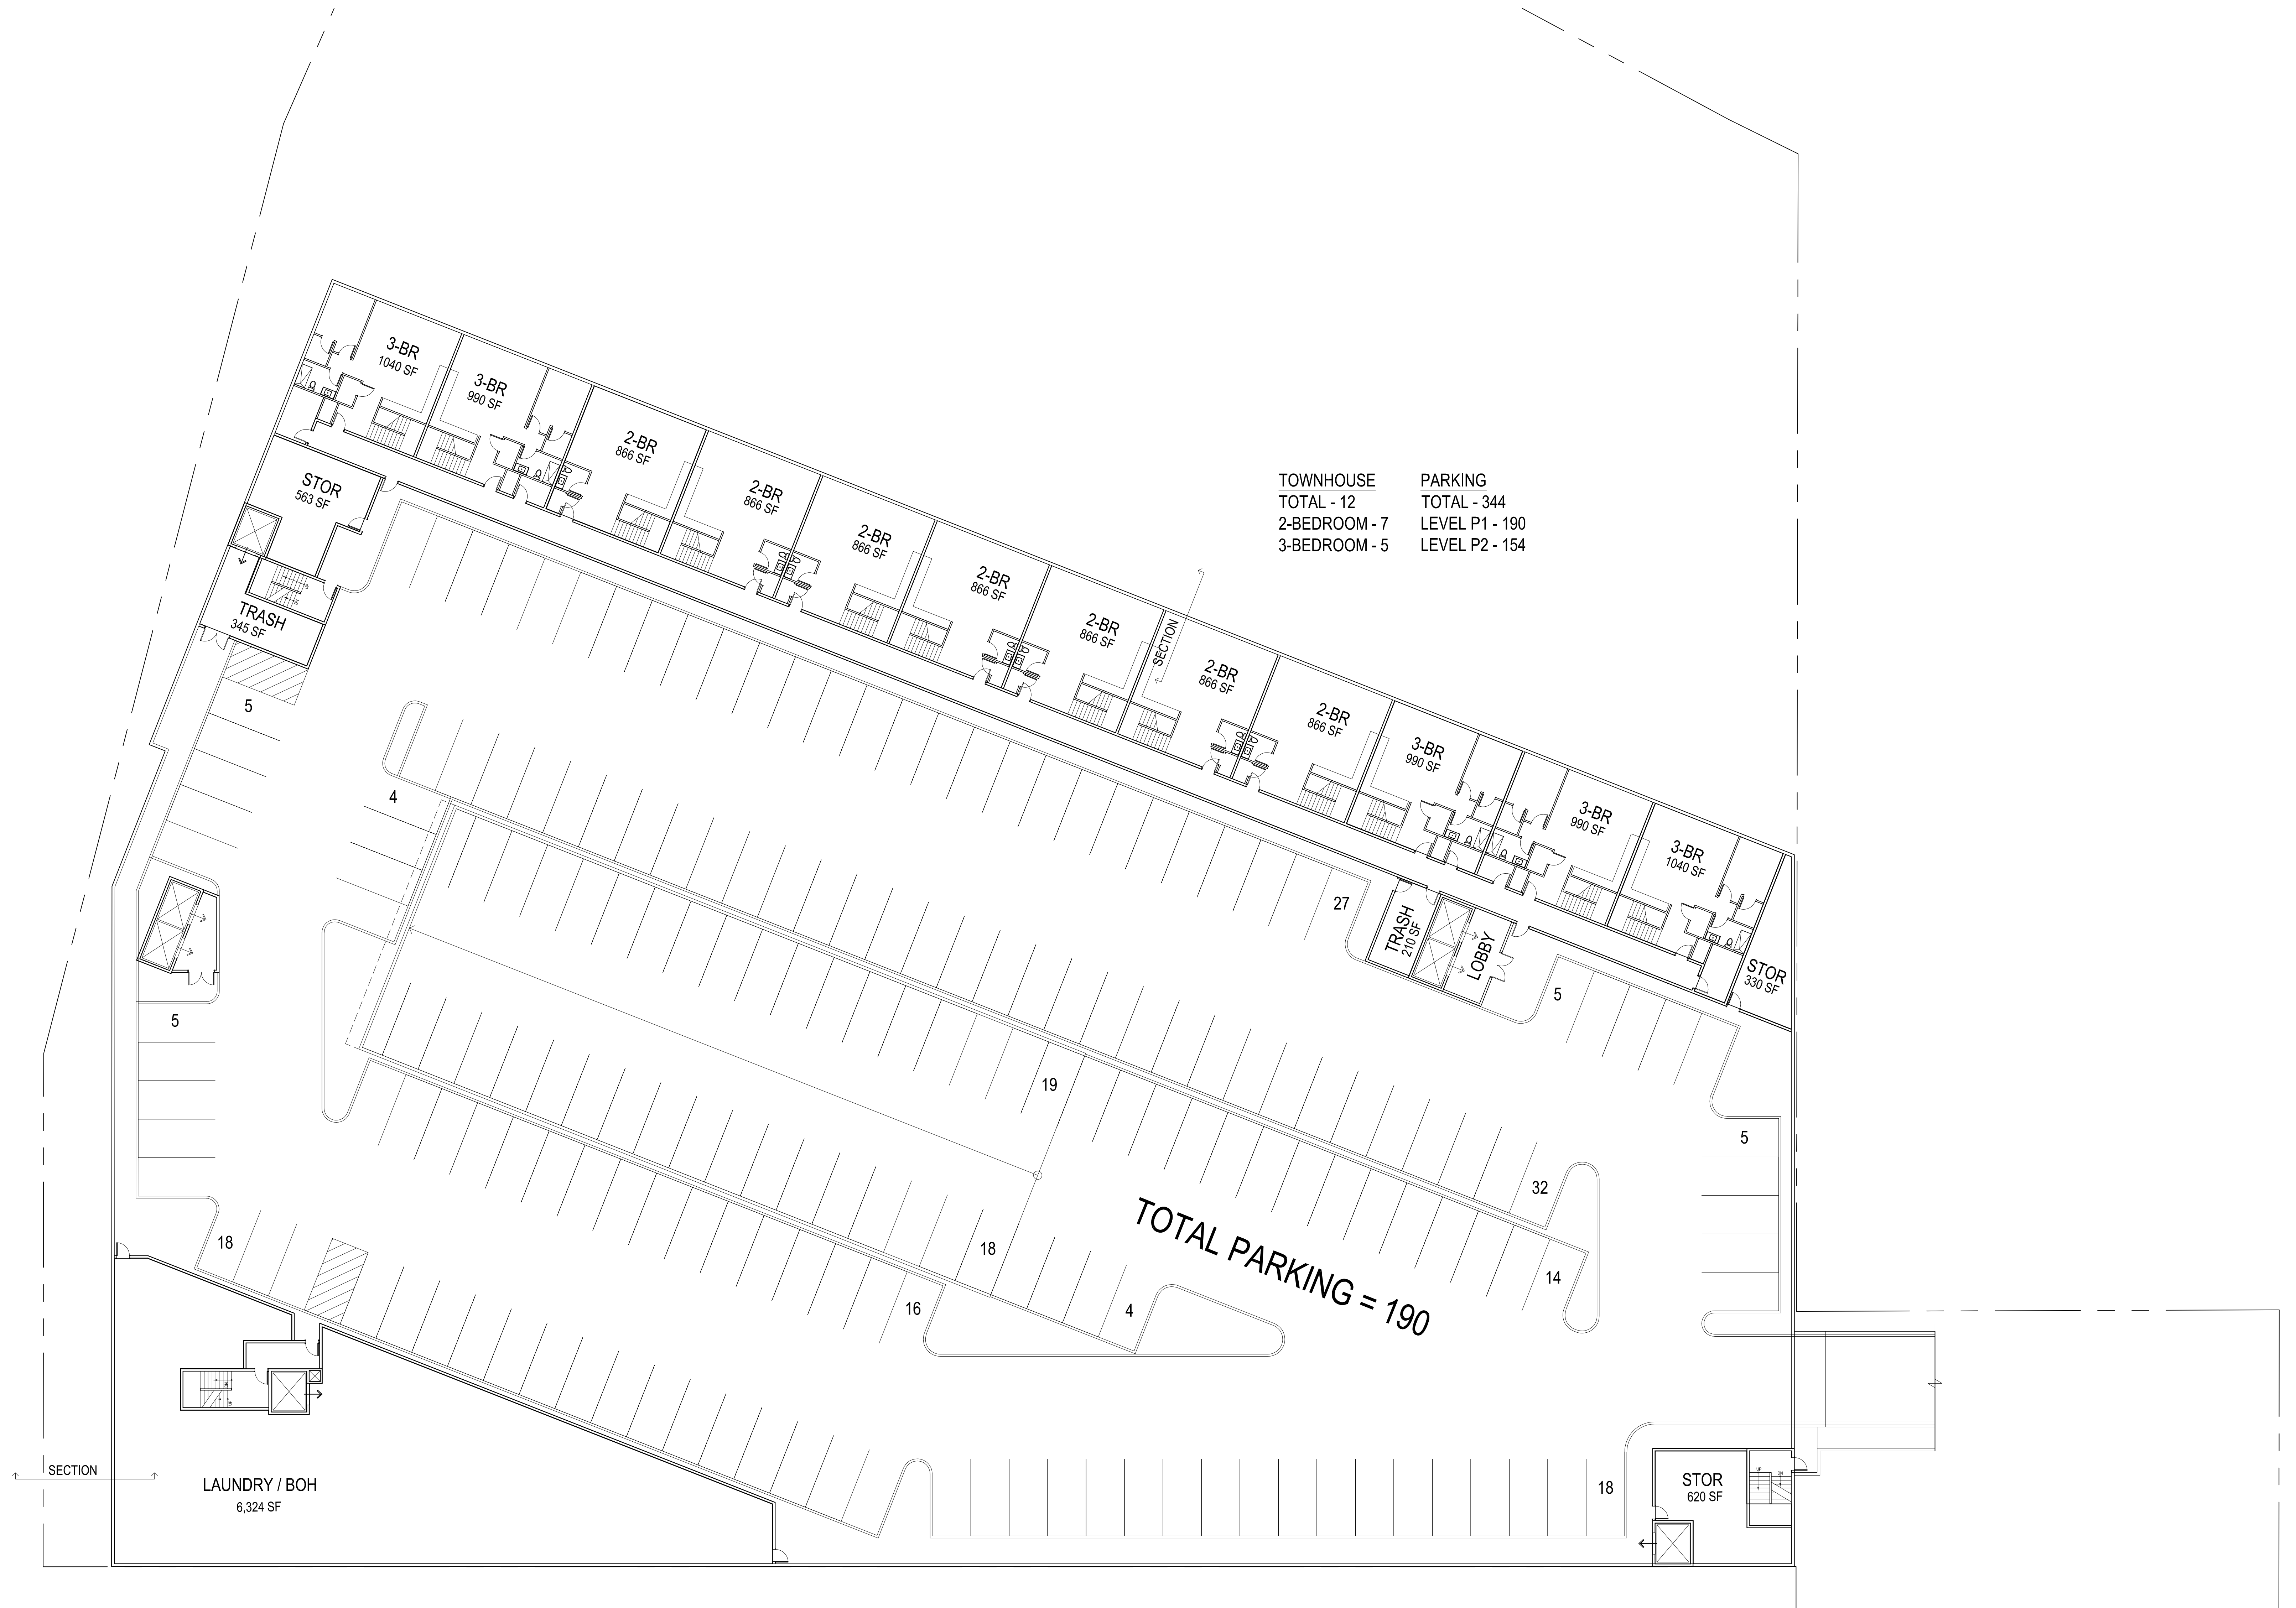

LEVEL P1 - GARAGE

HIGGINS WATERFRONT

SCALE: 1/16" = 1'-0"

MISSOULA, MT

JENSEN DAVENPORT ARCHITECTS, INC.
 architecture | planning | interior design
 14421 Woodinville Redmond Rd NE, Woodinville, WA 98072

HOTEL CONCEPT + CONDO SD SET 03.13.2026




LEVEL 1

HIGGINS WATERFRONT

SCALE: 1/16" = 1'-0"

MISSOULA, MT

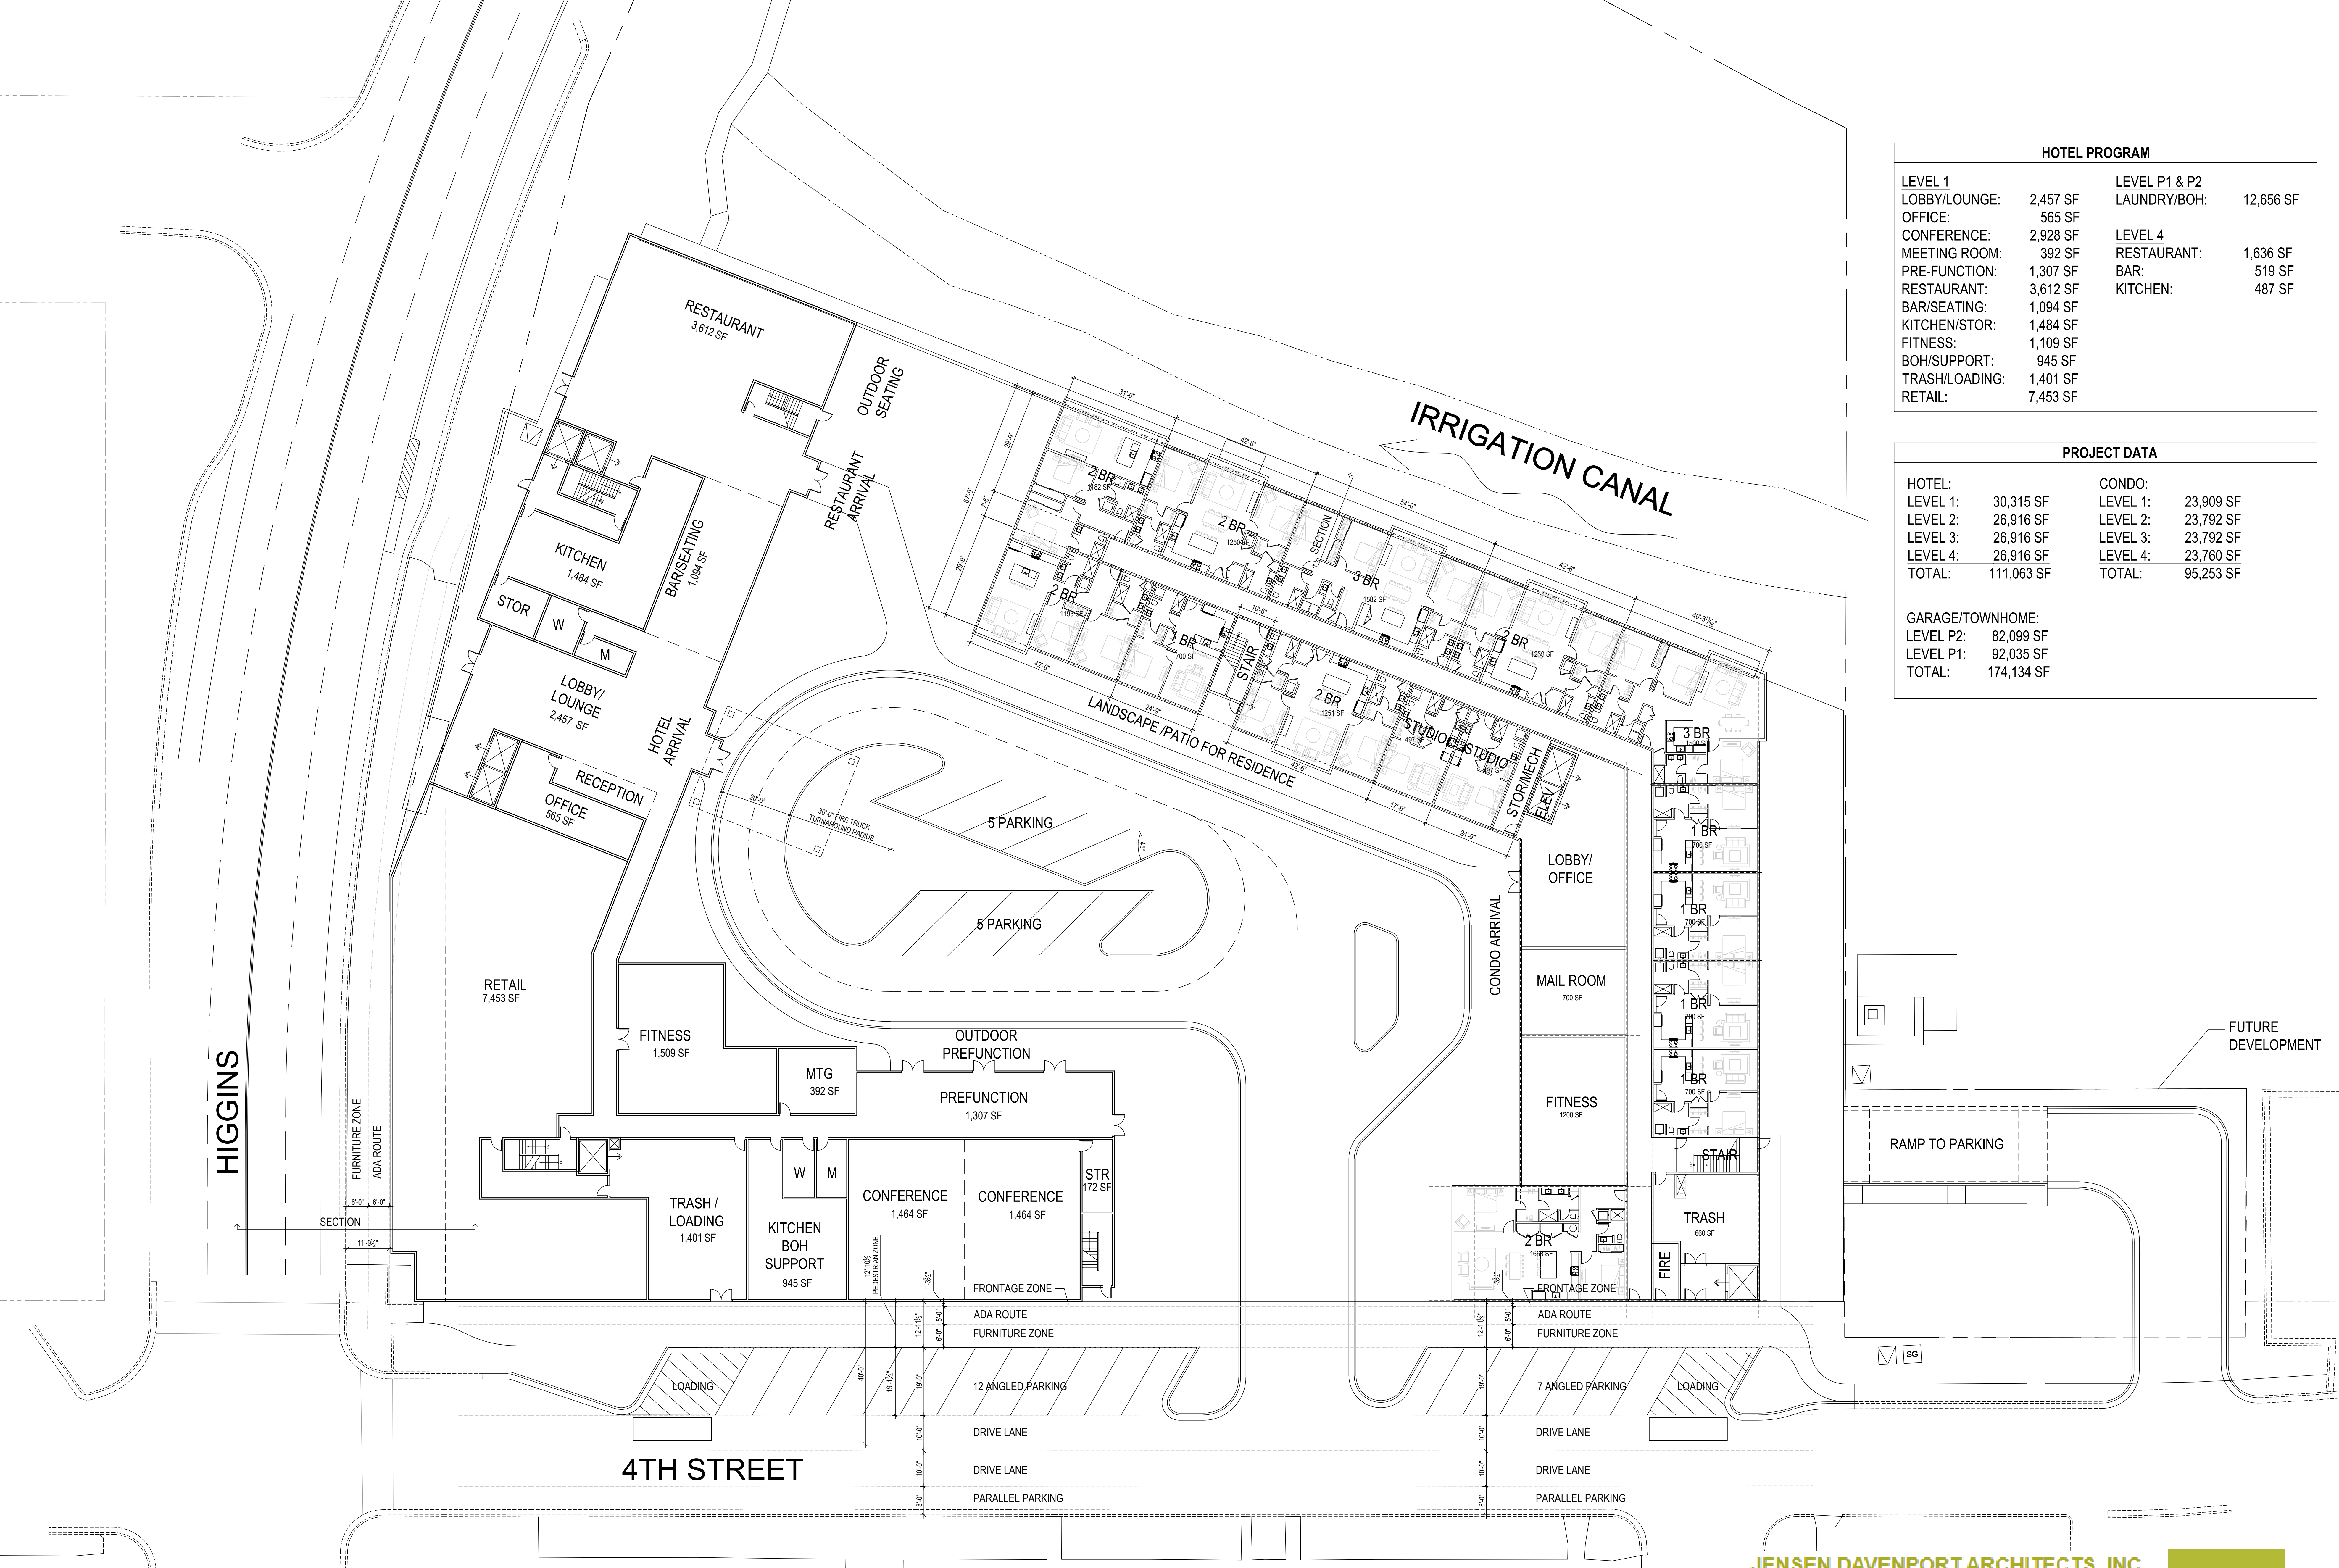

HOTEL PROGRAM			
LEVEL 1		LEVEL P1 & P2	
LOBBY/LOUNGE:	2,457 SF	LAUNDRY/BOH:	12,656 SF
OFFICE:	565 SF		
CONFERENCE:	2,928 SF	LEVEL 4	
MEETING ROOM:	392 SF	RESTAURANT:	1,636 SF
PRE-FUNCTION:	1,307 SF	BAR:	519 SF
RESTAURANT:	3,612 SF	KITCHEN:	487 SF
BAR/SEATING:	1,094 SF		
KITCHEN/STOR:	1,484 SF		
FITNESS:	1,109 SF		
BOH/SUPPORT:	945 SF		
TRASH/LOADING:	1,401 SF		
RETAIL:	7,453 SF		

PROJECT DATA			
HOTEL:		CONDO:	
LEVEL 1:	30,315 SF	LEVEL 1:	23,909 SF
LEVEL 2:	26,916 SF	LEVEL 2:	23,792 SF
LEVEL 3:	26,916 SF	LEVEL 3:	23,792 SF
LEVEL 4:	26,916 SF	LEVEL 4:	23,760 SF
TOTAL:	111,063 SF	TOTAL:	95,253 SF
GARAGE/TOWNHOME:			
LEVEL P2:	82,099 SF		
LEVEL P1:	92,035 SF		
TOTAL:	174,134 SF		

LEVEL 2-3

HIGGINS WATERFRONT

SCALE: 1/16" = 1'-0"

MISSOULA, MT

JENSEN DAVENPORT ARCHITECTS, INC.
architecture | planning | interior design
14421 Woodinville Redmond Rd NE, Woodinville, WA 98072

HOTEL CONCEPT + CONDO SD SET 03.13.2026



GUESTROOM MATRIX				
ROOM TYPE	LEVELS			TOTAL
	2	3	4	
SINGLE KING	33	33	33	99
DOUBLE QUEEN	18	18	13	49
SUITE	2	2	0	4
JR SUITE	3	3	3	9
TOTAL	56	56	49	161

TOTAL FLOOR SF = 26,949 SF

CONDO UNIT MATRIX					
# OF BEDROOM	LEVELS				TOTAL
	1	2	3	4	
STUDIO	2	0	0	0	2
1 BEDROOM	5	7	7	0	19
2 BEDROOM	6	9	9	5	29
3 BEDROOM	2	2	2	3	9
3 BED + DEN	0	0	0	2	2
4 BEDROOM	0	0	0	2	2
TOTAL	15	18	18	12	63

GUESTROOM MATRIX				
ROOM TYPE	LEVELS			TOTAL
	2	3	4	
SINGLE KING	33	33	33	99
DOUBLE QUEEN	18	18	13	49
SUITE	2	2	0	4
JR SUITE	3	3	3	9
TOTAL	56	56	49	161

TOTAL FLOOR SF = 26,949 SF

LEVEL 4


HIGGINS WATERFRONT


SCALE: 1/16" = 1'-0"

MISSOULA, MT

JENSEN DAVENPORT ARCHITECTS, INC.
architecture | planning | interior design
14421 Woodinville Redmond Rd NE, Woodinville, WA 98072

HOTEL CONCEPT + CONDO SD SET 03.13.2026

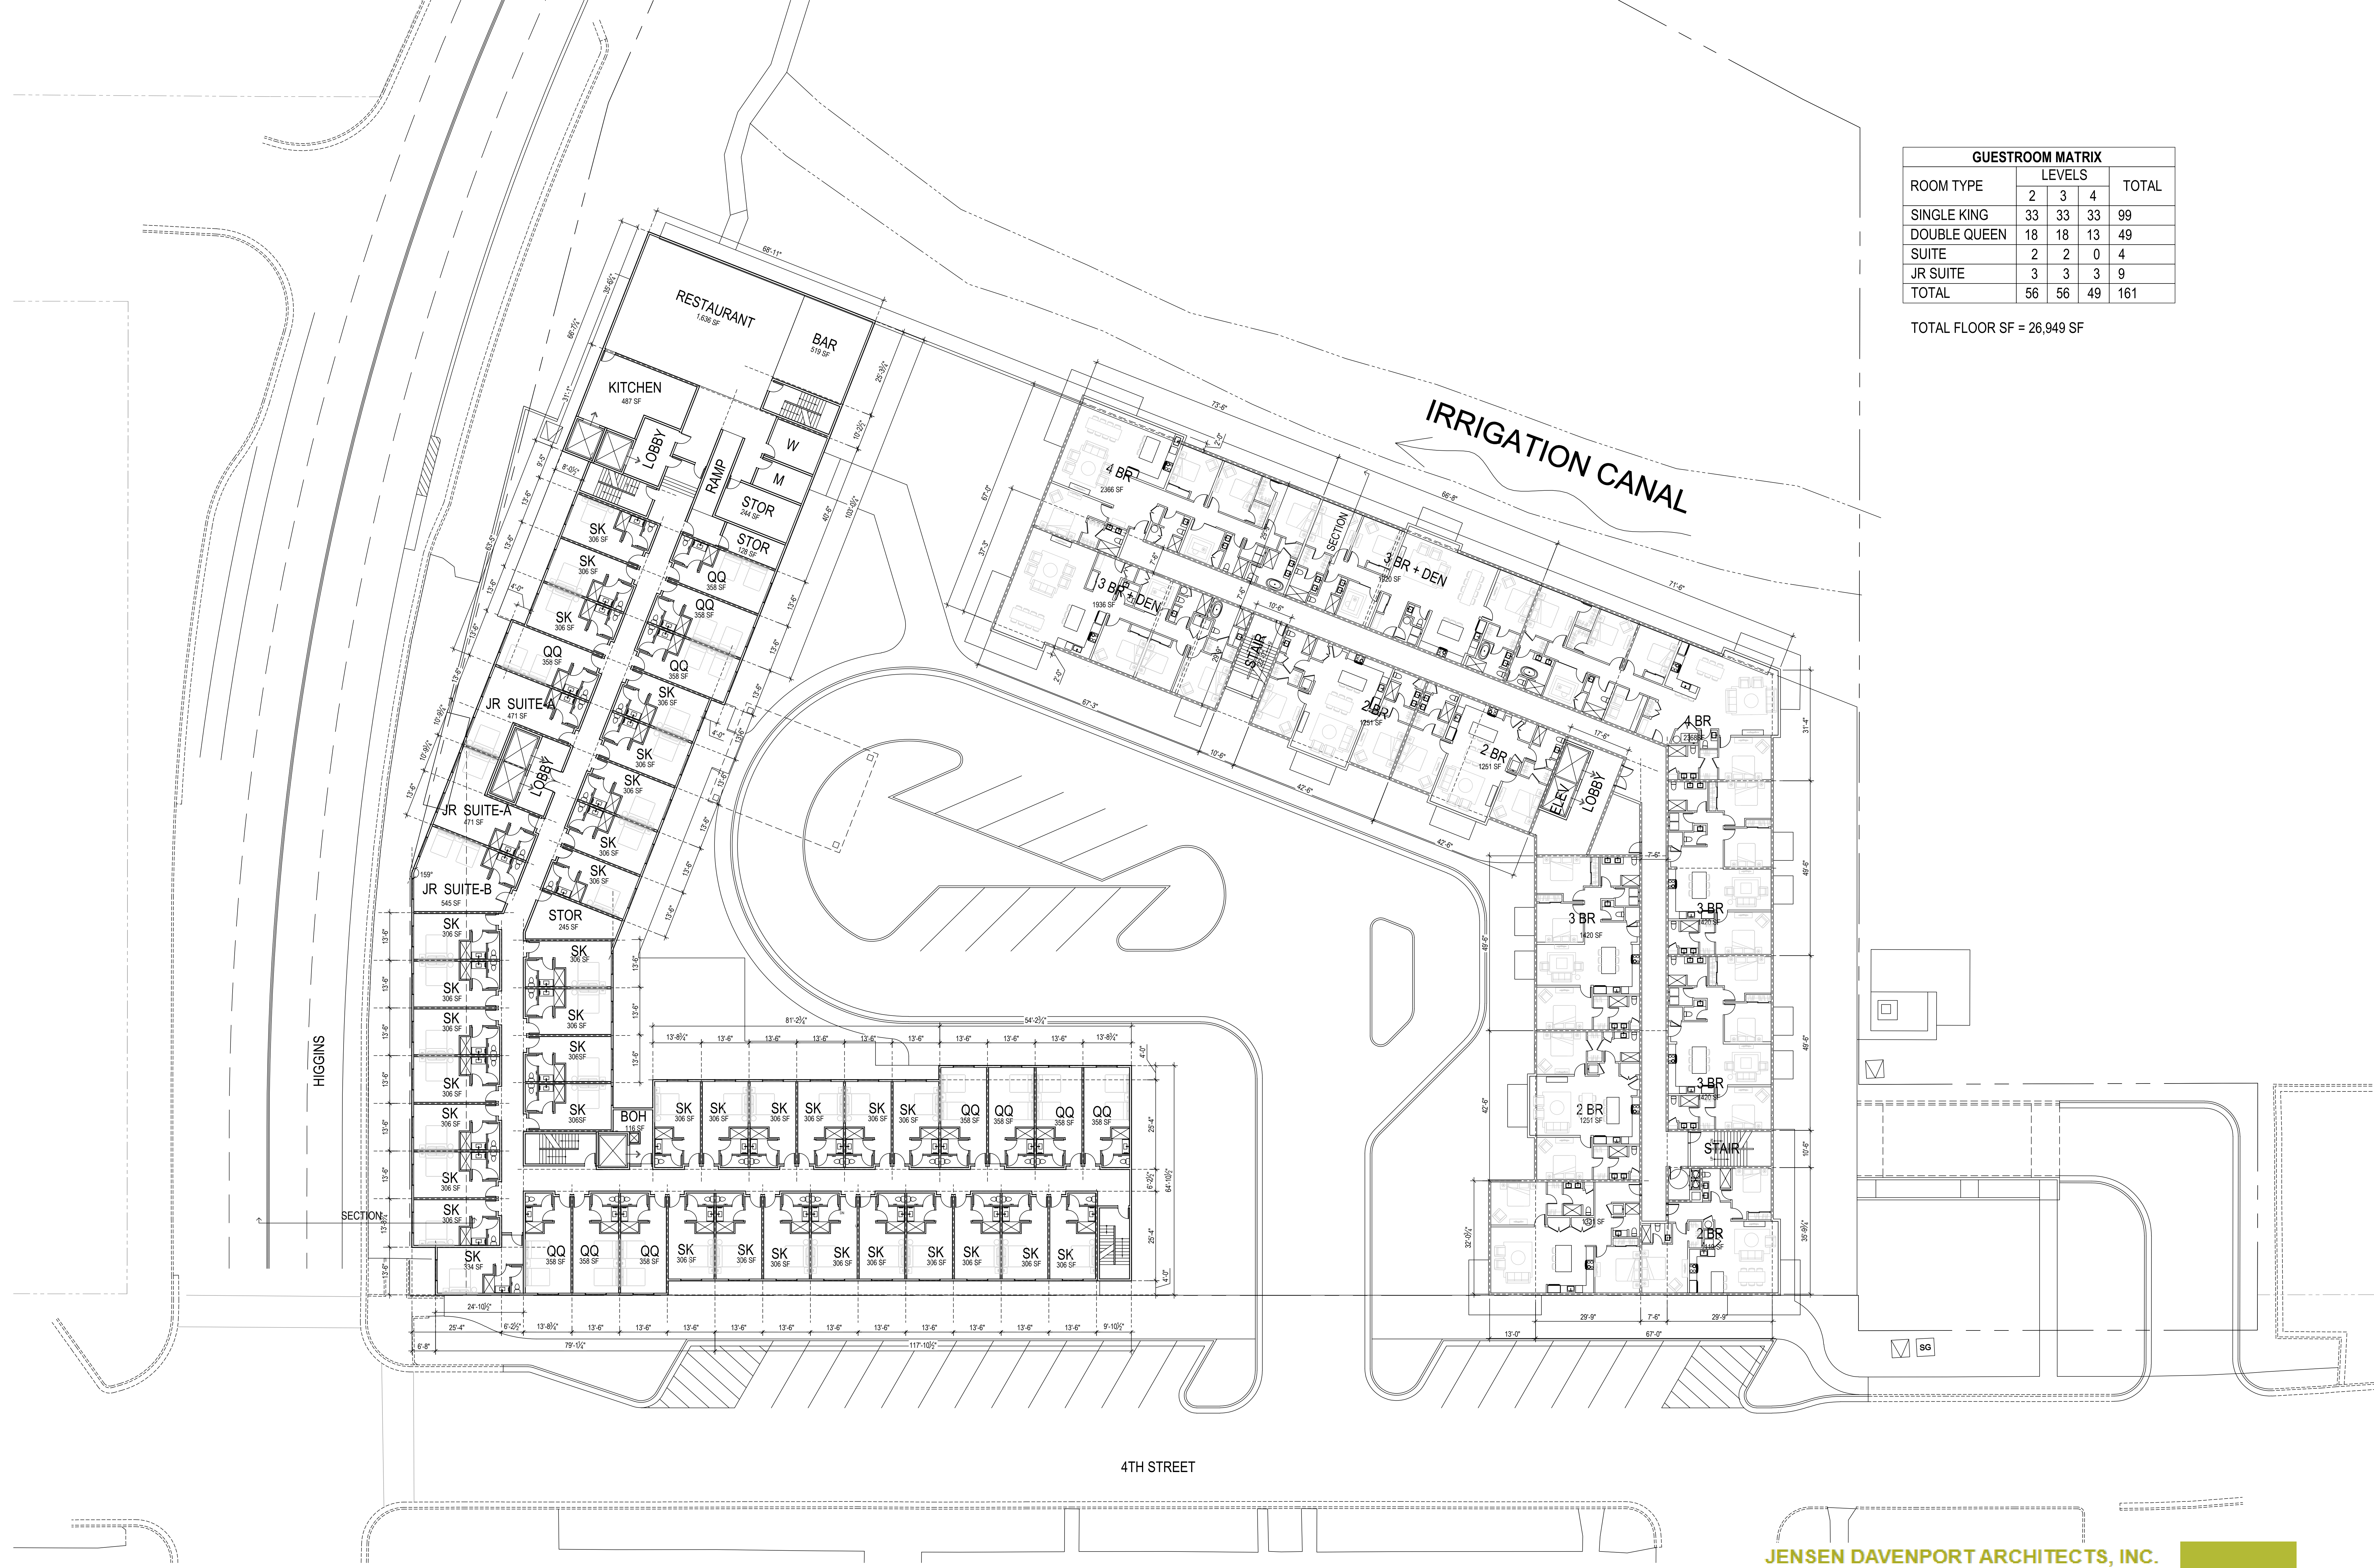

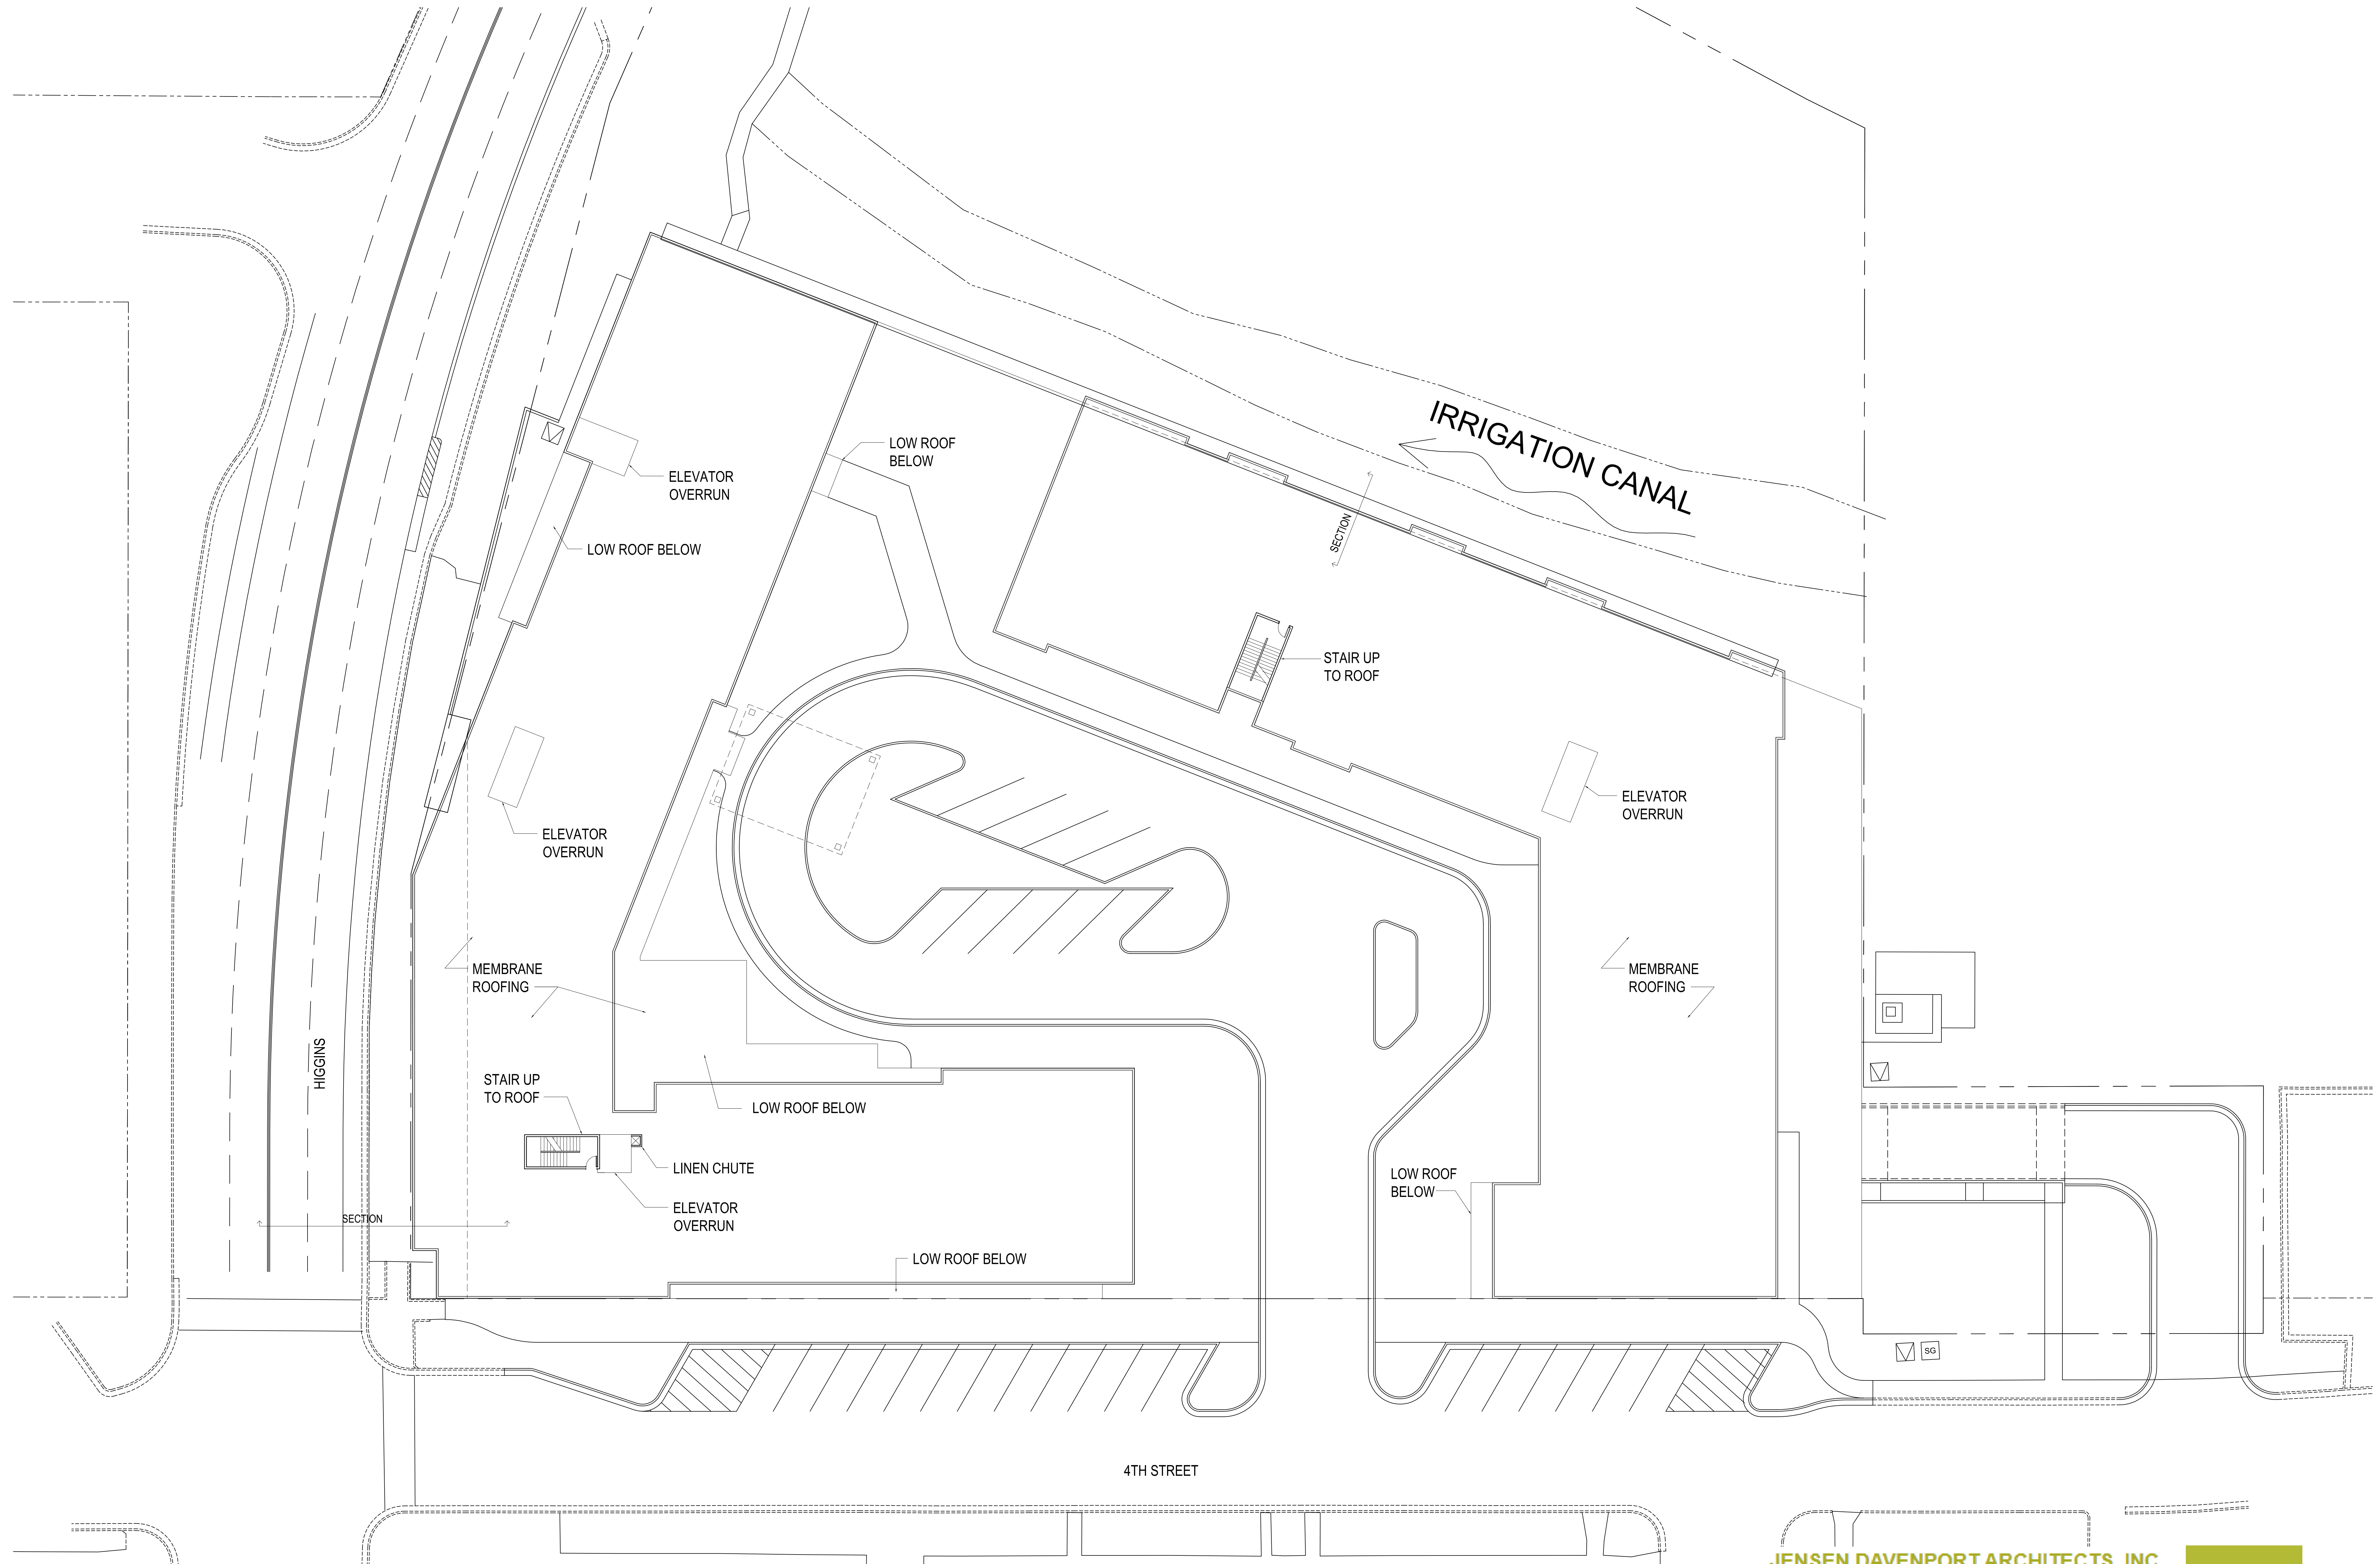

ROOF

HIGGINS WATERFRONT


SCALE: 1/16" = 1'-0"

MISSOULA, MT

JENSEN DAVENPORT ARCHITECTS, INC.
 | architecture | planning | interior design
 14421 Woodinville Redmond Rd NE, Woodinville, WA 98072

HOTEL CONCEPT + CONDO SD SET 03.13.2026



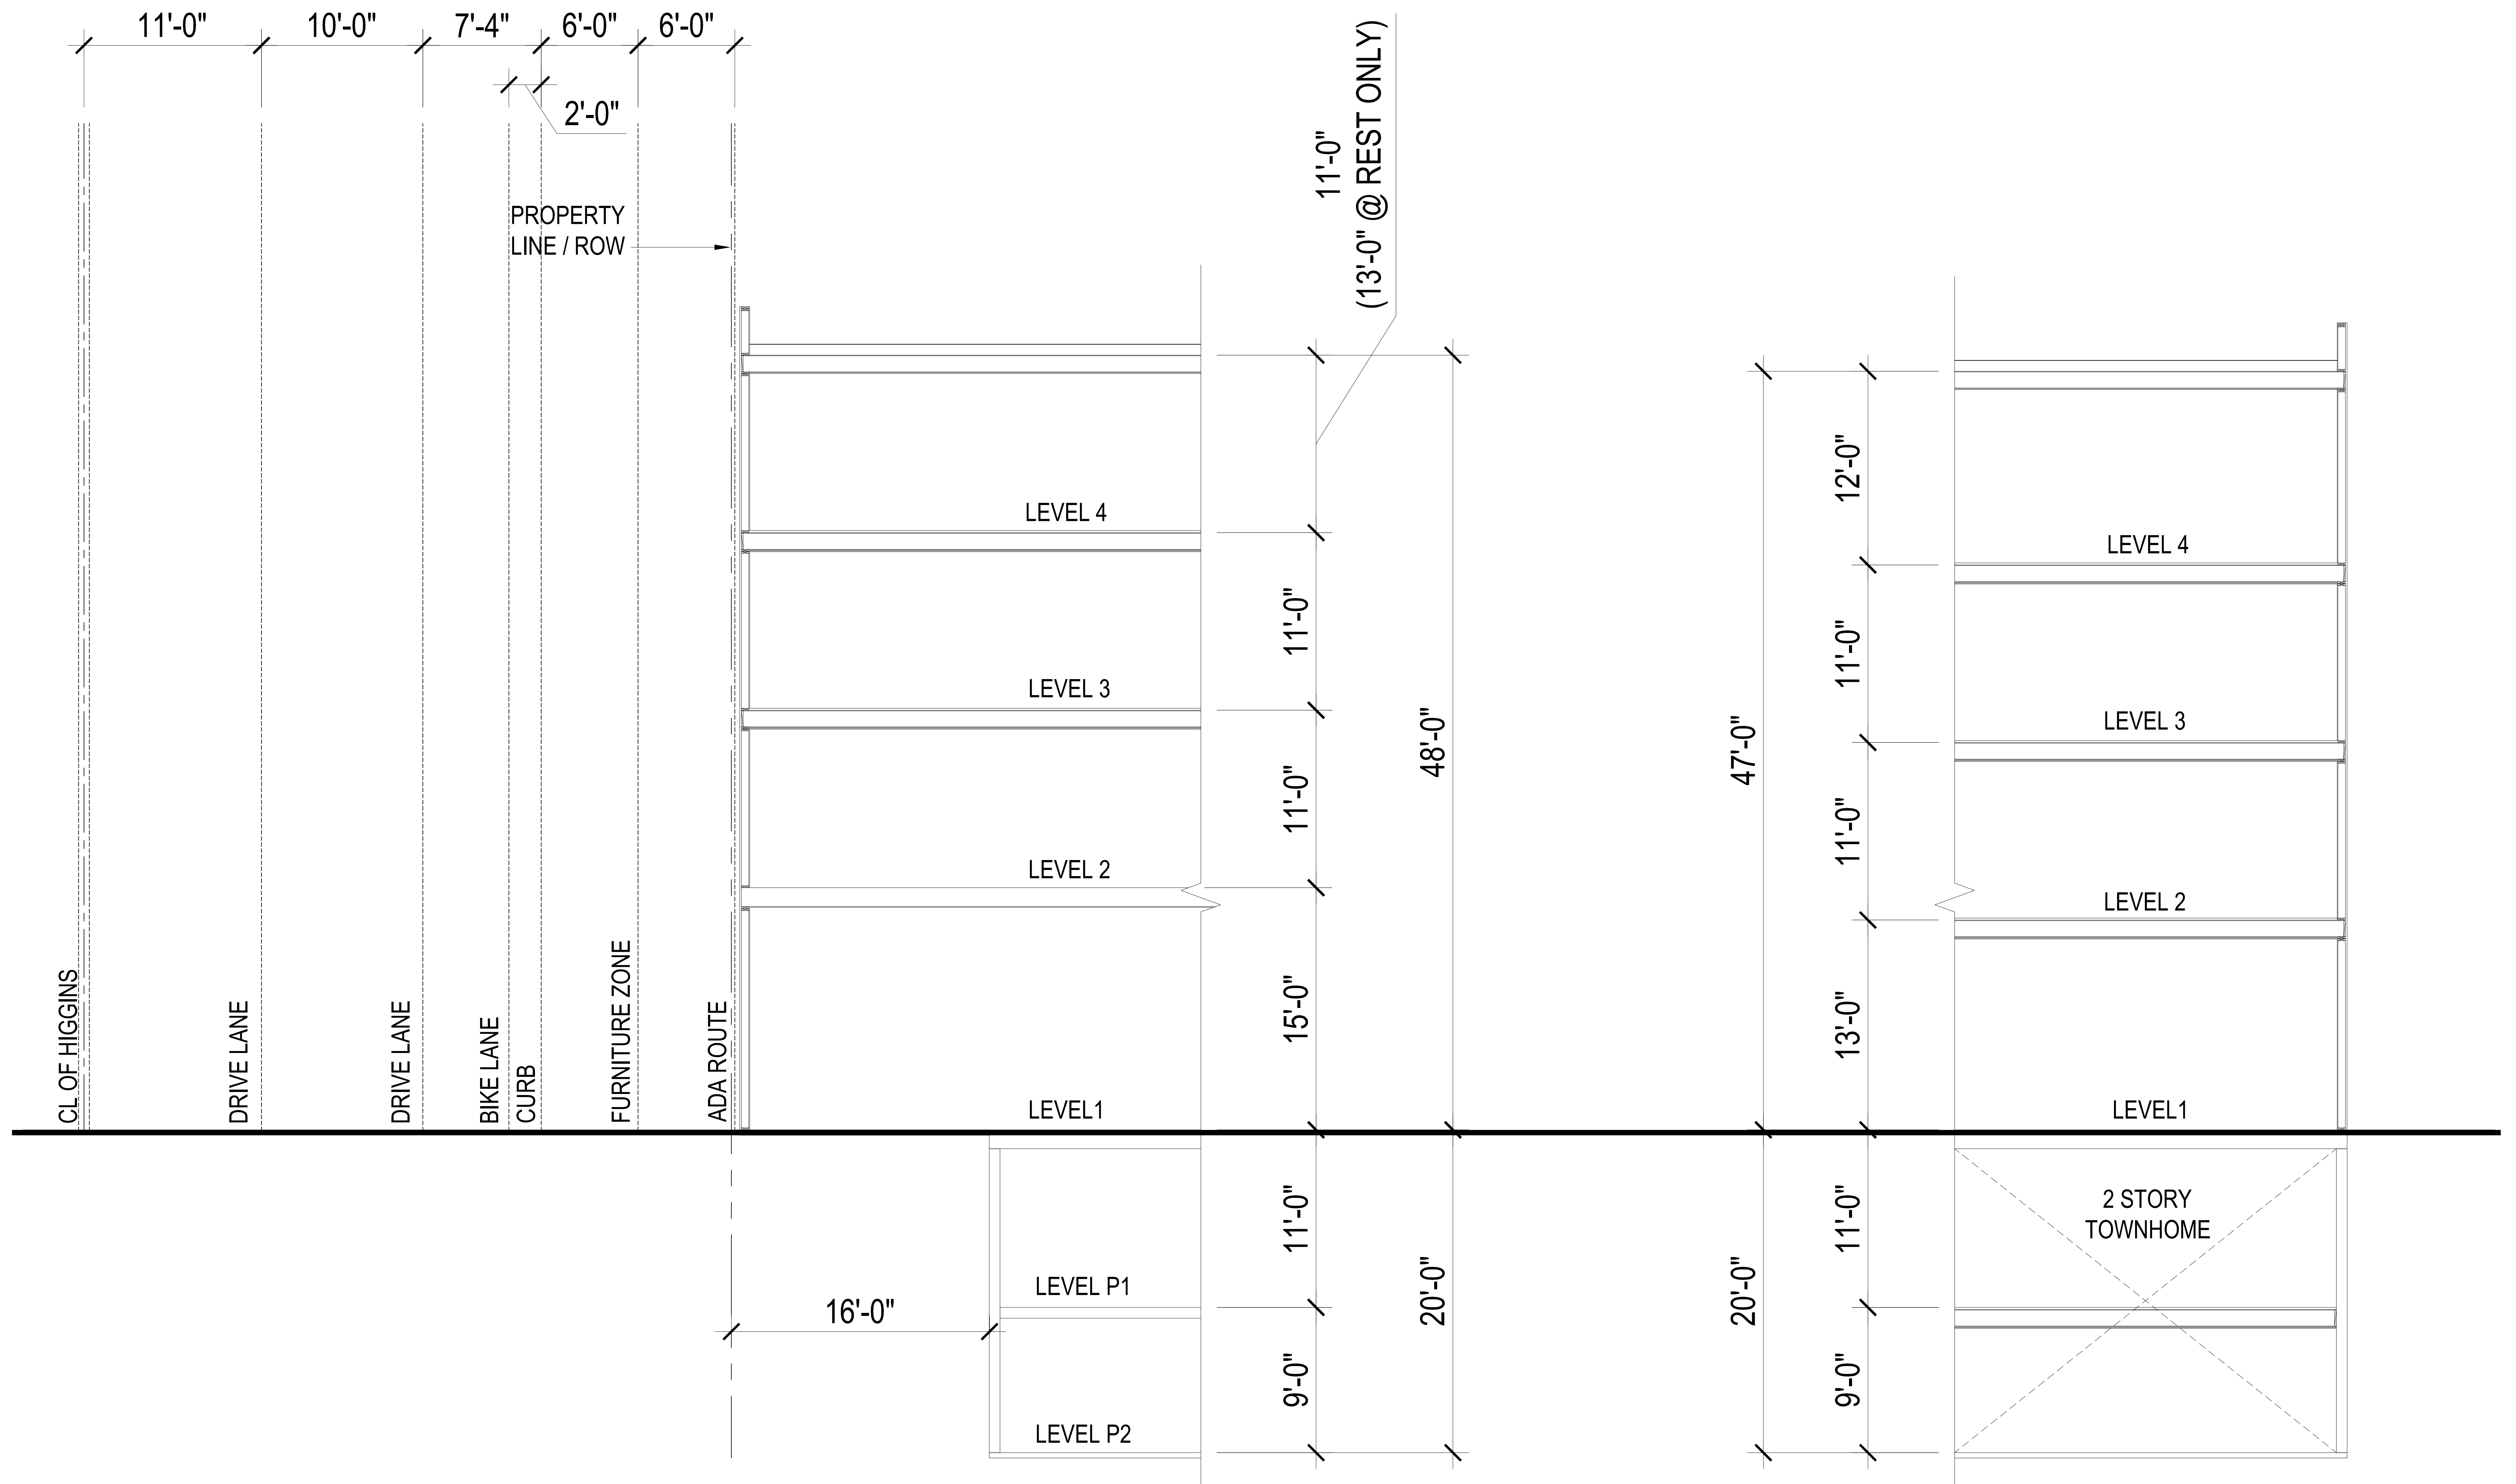

TYPICAL HOTEL SECTION

TYPICAL CONDO SECTION

BUILDING SECTIONS

HIGGINS WATERFRONT


SCALE: 1/4" = 1'-0"

MISSOULA, MT

JENSEN DAVENPORT ARCHITECTS, INC.
architecture | planning | interior design
14421 Woodinville Redmond Rd NE, Woodinville, WA 98072

HOTEL CONCEPT + CONDO SD SET 03.13.2026



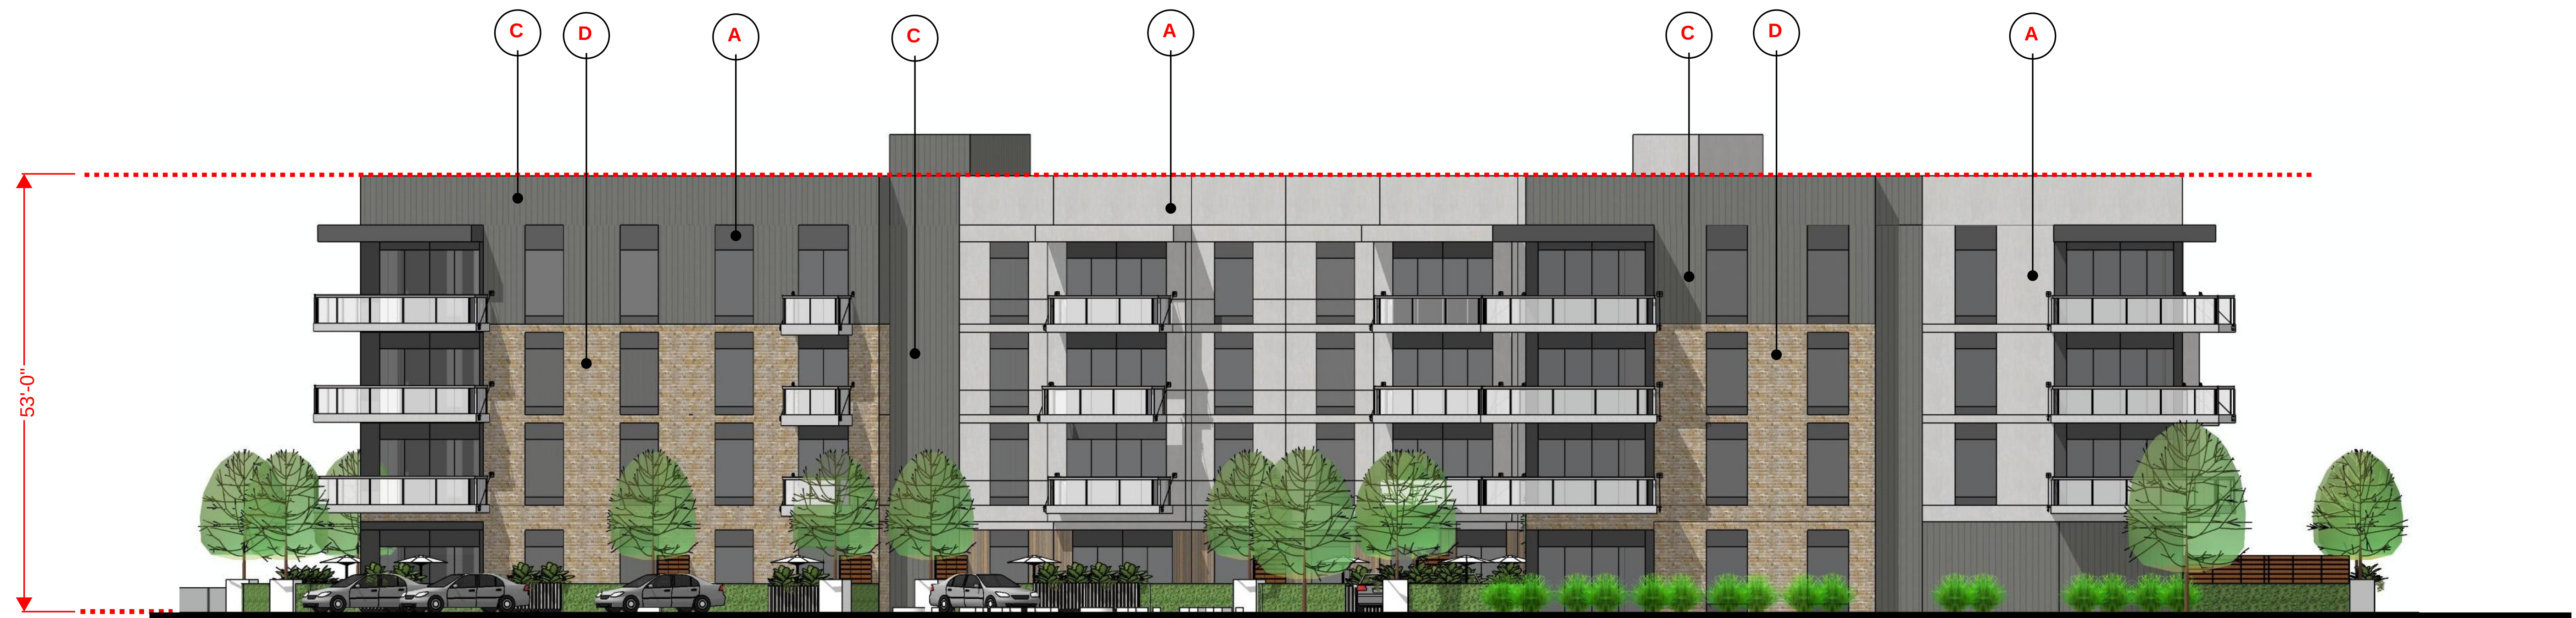


SOUTH ELEVATION

A



FIBER CEMENT PANELS
(APPRX. 45% OF FACADE AREA)

B

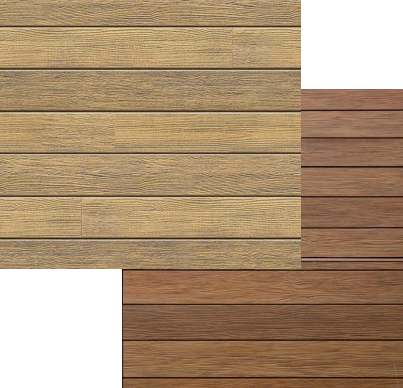

"FAUX WOOD"
FIBER CEMENT PANELS
(APPRX. 4% OF FACADE AREA)

C



CORRUGATED METAL
PANELS
(APPRX. 18% OF FACADE AREA)

D



BRICK
(APPRX. 8% OF FACADE AREA)

GLAZING
(APPRX. 25% OF FACADE AREA)



NORTH ELEVATION

BUILDING ELEVATIONS

HIGGINS WATERFRONT

SCALE: 3/32" = 1'-0"

MISSOULA, MT

JENSEN DAVENPORT ARCHITECTS, INC.
architecture | planning | interior design
14421 Woodinville Redmond Rd NE, Woodinville, WA 98072


HOTEL CONCEPT + CONDO SD SET 03.13.2026






EAST ELEVATION

A

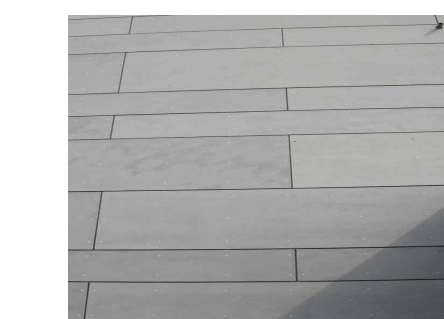


FIBER CEMENT PANELS
(APPRX. 45% OF FACADE AREA)

B

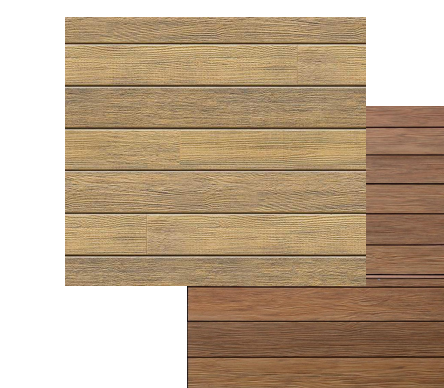


"FAUX WOOD"
FIBER CEMENT PANELS
(APPRX. 4% OF FACADE AREA)

C

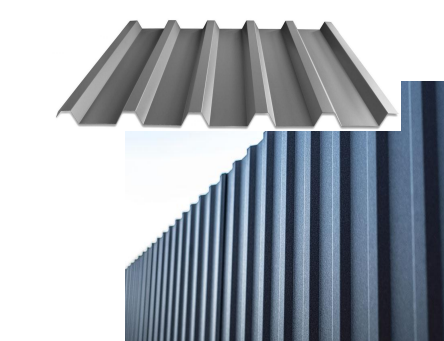

CORRUGATED METAL
PANELS
(APPRX. 18% OF FACADE AREA)

D

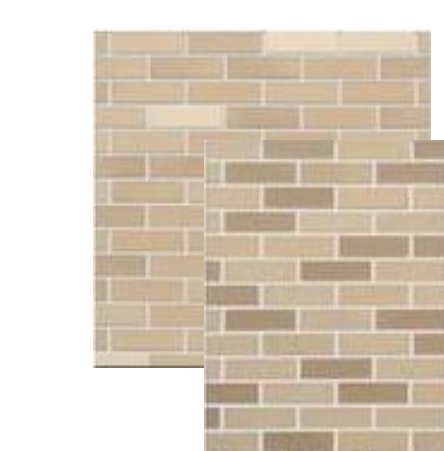

BRICK
(APPRX. 8% OF FACADE AREA)

GLAZING
(APPRX. 25% OF FACADE AREA)



WEST ELEVATION

BUILDING ELEVATIONS

HIGGINS WATERFRONT

SCALE: 3/32" = 1'-0"

MISSOULA, MT

JENSEN DAVENPORT ARCHITECTS, INC.
architecture | planning | interior design
14421 Woodinville Redmond Rd NE, Woodinville, WA 98072

HOTEL CONCEPT + CONDO SD SET 03.13.2026





COURTYARD VIEWS



BUILDING PERSPECTIVES



NORTHEAST VIEWS



BUILDING PERSPECTIVES

HIGGINS WATERFRONT

MISSOULA, MT

JENSEN DAVENPORT ARCHITECTS, INC.
 architecture | planning | interior design
 14421 Woodinville Redmond Rd NE, Woodinville, WA 98072

HOTEL CONCEPT + CONDO SD SET 03.13.2026





NORTH VIEWS



BUILDING PERSPECTIVES

HIGGINS WATERFRONT

MISSOULA, MT

JENSEN DAVENPORT ARCHITECTS, INC.
 architecture | planning | interior design
 14421 Woodinville Redmond Rd NE, Woodinville, WA 98072

HOTEL CONCEPT + CONDO SD SET 03.13.2026

